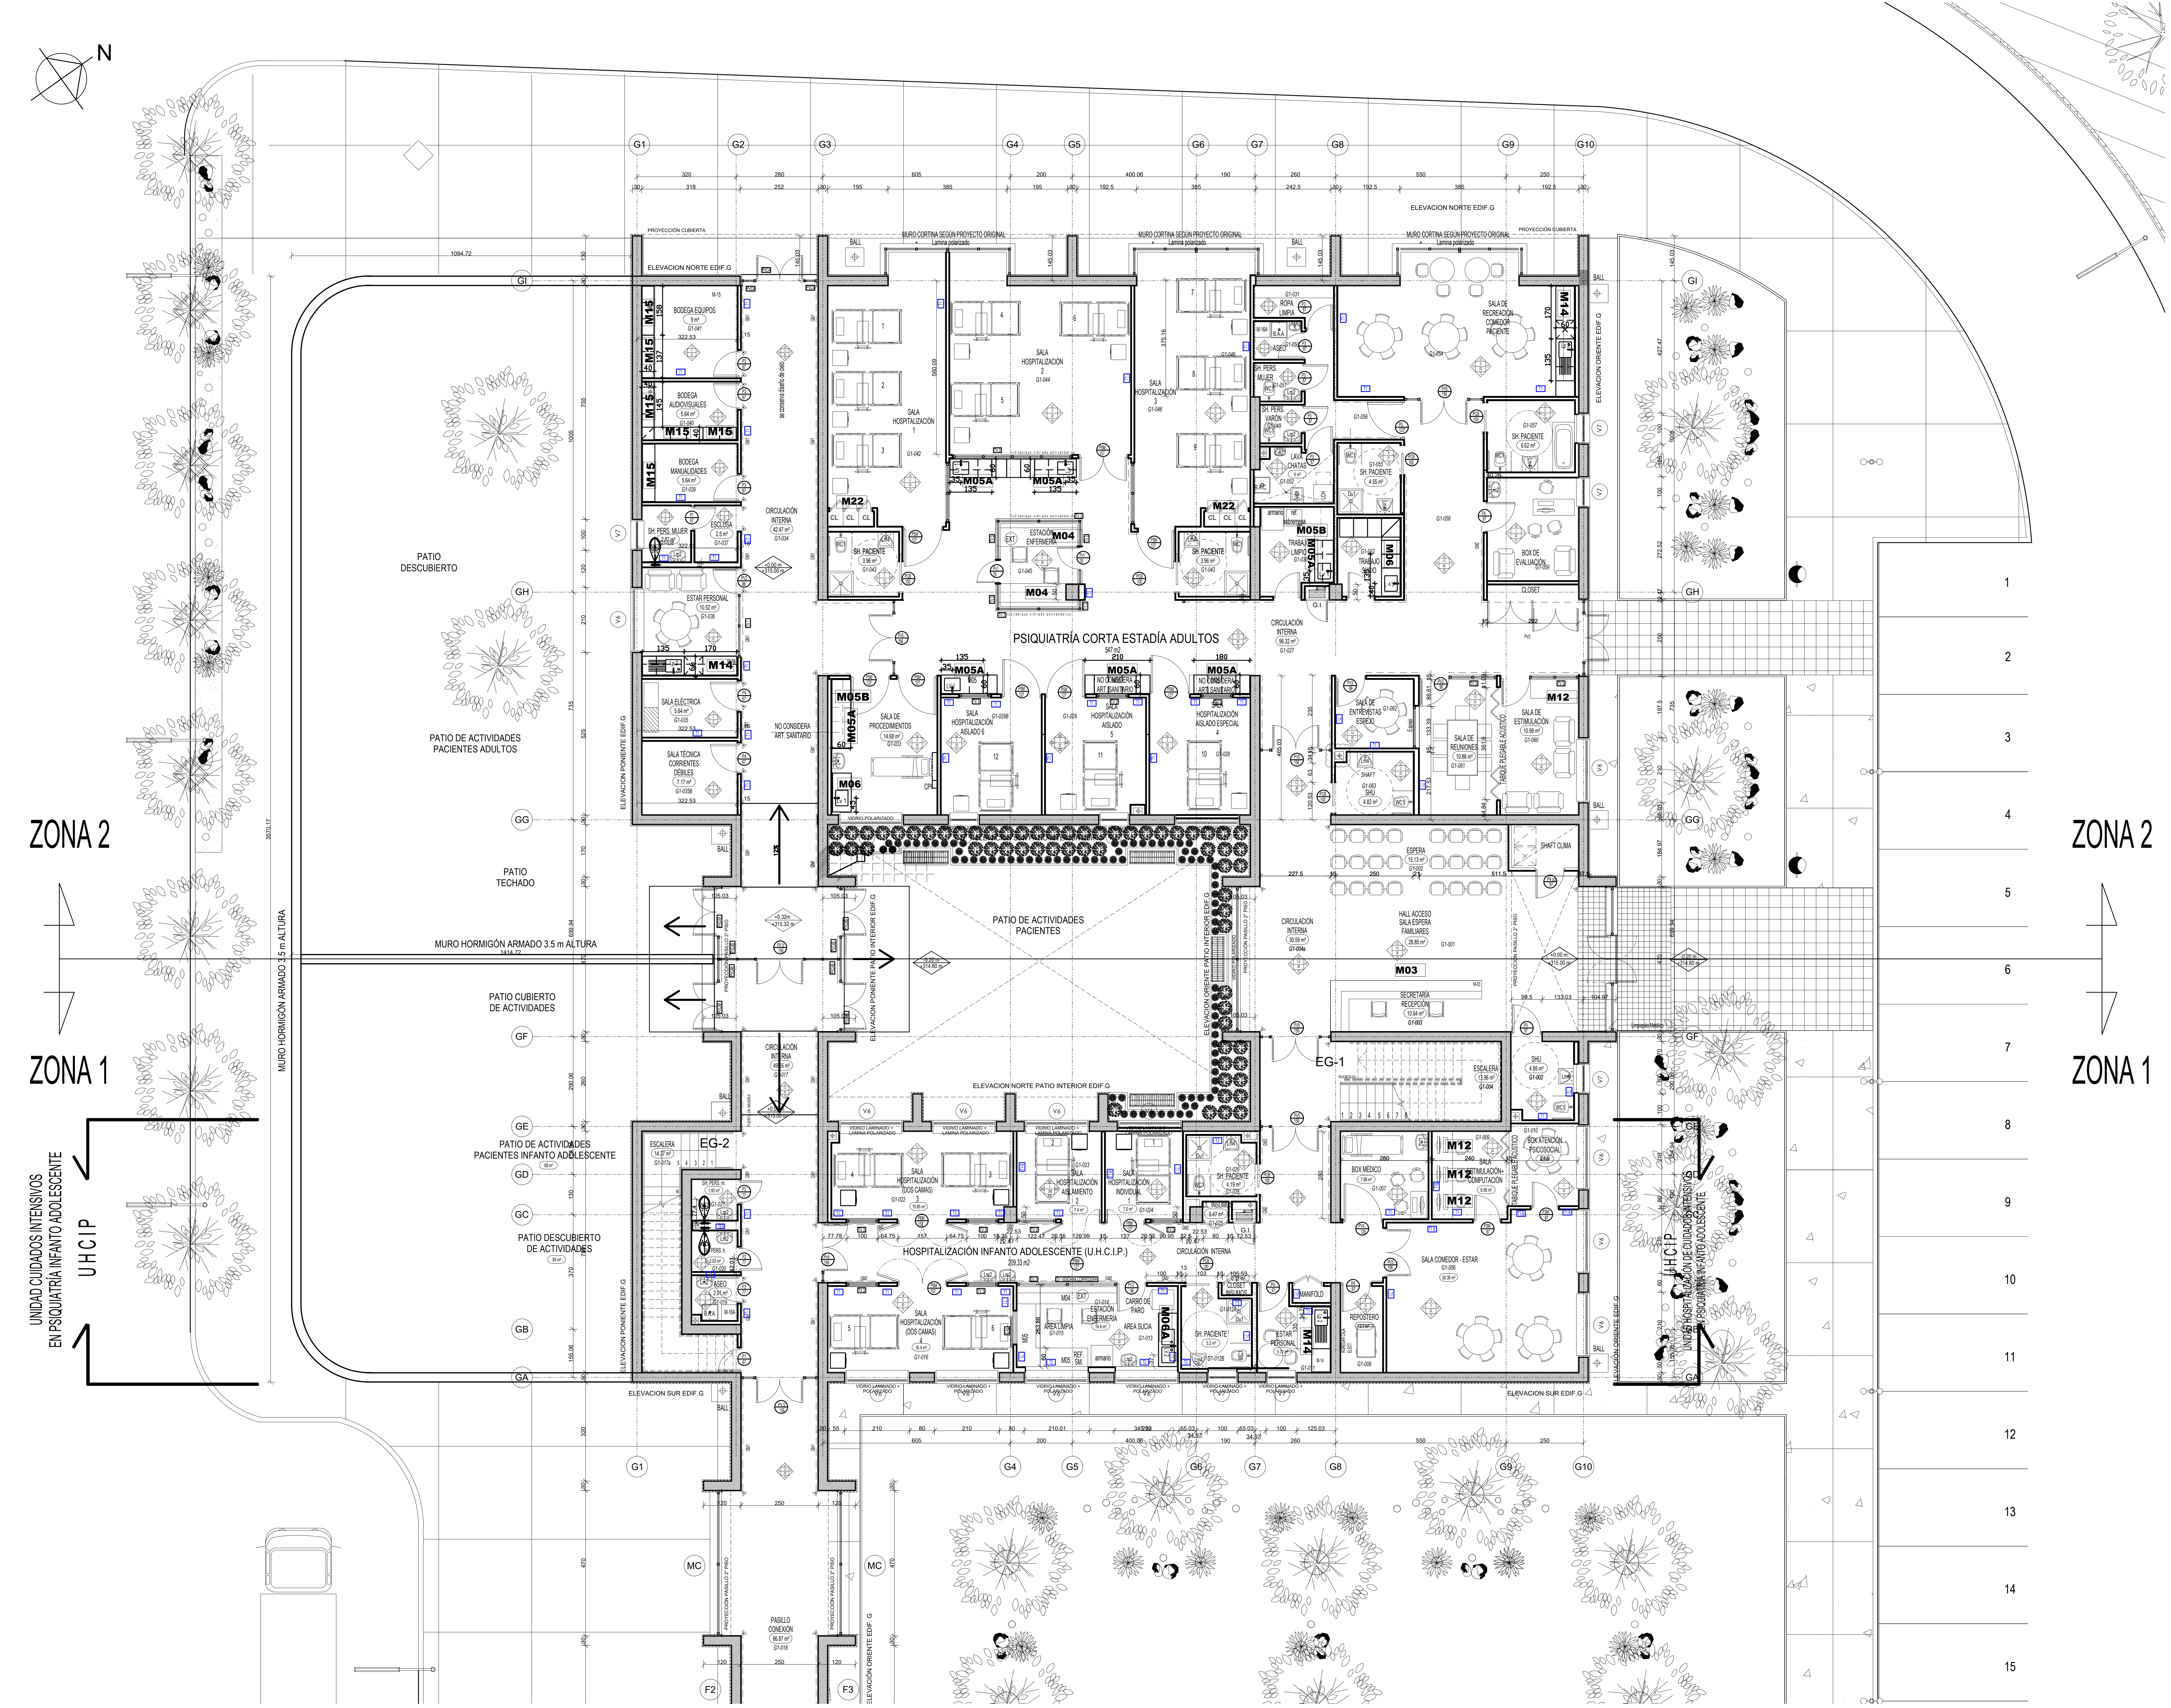
N
G1
G2
G3
G4
G5
G6
G7
G8
G9
G10
GI
GH
GG
GF
GE
GD
GC
GB
GA
ELEVACION NORTE EDIF. G
ZONA 2
ZONA 1
PATIO DESCUBIERTO
PATIO DE ACTIVIDADES PACIENTES ADULTOS
PATIO TECHADO
MURO HORMIGÓN ARMADO 3.5 m ALTURA
PATIO CUBIERTO DE ACTIVIDADES
PATIO DE ACTIVIDADES PACIENTES INFANTO ADOLESCENTE
PATIO DESCUBIERTO DE ACTIVIDADES
UNIDAD CUIDADOS INTENSIVOS EN PSIQUIATRÍA INFANTO ADOLESCENTE
U H C I P
PSIQUIATRÍA CORTA ESTADÍA ADULTOS
PATIO DE ACTIVIDADES PACIENTES
HALL ACCESO SALA ESPERA FAMILIARES
HOSPITALIZACIÓN INFANTO ADOLESCENTE (U.H.C.I.P.)
SALA COMEDOR - ESTAR
SALA DE RECREACIÓN COMEDOR PACIENTE
BOX DE EVALUACIÓN
SALA DE ESTIMULACIÓN
SALA DE REUNIONES
SALA DE PROCEDIMIENTOS
SALA HOSPITALIZACIÓN
ESTACIÓN ENFERMERÍA
CIRCULACIÓN INTERNA
SECRETARÍA RECEPCIÓN
ESPERA
EG-1
EG-2
PASILLO CONEXIÓN
ELEVACION SUR EDIF. G
ELEVACION PONIENTE EDIF. G
ELEVACION ORIENTE EDIF. G
1
2
3
4
5
6
7
8
9
10
11
12
13
14
15

Planta Edif. G, 1º Piso

ESCALA 1:75

SIMBOLOGIA

SIMBOLOGIA GENERAL

A2-101 :Numero recinto
+0.00 / 107.00 :Cota nivel N.P.T.
+4.20 :Nivel obra gruesa
+4.20 :Nivel obra terminada
C.J.P. :Cubre Junta Piso
2 / 1-035 :Simbología de corte, escantillon o detalle
Pb :Forro plomo
TV1 :Tabique vidriado
P1 / 80 :Puerta opaca
PV1 / 80 :Puerta vidriada
PP1 / 80 :Puerta vidriada Protex
PC / 80 :Puerta metálica
PCM / 80 :Puerta corredera metálica
PCB / 100 :Puerta corredera baño
PCC / 80 :Puerta corredera pabellón
PCF / 80 :Puerta cortafuego
V1 :Tipo ventana
PCL2 :Closet
PM1 :Pasamuro
E :Escape
RJ :Reloj
◎ :Bola antichoque (acceso ambulancia)
AP : Abre puerta
GM1 :Guarda muro pasamano
GM2 :Guarda muro adosado
:Cantonera
BR1 :Baranda
M57 :Mueble adosado N°
:Bajada aguas lluvias, BALL
:Ventilacion o descarga alcantarillado
:Muros, pilares, obra gruesa
:Pendiente pavimento
CPI :Canaleta porta instalaciones, CPI
TE :Tablero eléctrico
TCC :Tablero control centralizado
CAI :Central alarma incendio
AP :Closet control agua potable
SP :Closet control red roceadores
RS :Red seca
:Siamesa red húmeda (obras exteriores)
G.I. :Red húmeda (gabinete incendio)
CN :Estación correo neumático
SUM :Sumidero (obras exteriores)
GCL :Tablero de corte de gases clínicos
:Columnas clínicas retráctiles
:Carro RR.SS.
:Carro uso multiple 90x60cm Ropa sucia, ropa limpia, etc
:Camilla movil
:Mesa quirurgica
:Mesa ginecológica
:Cortina Divisora Ambiente
:Riel Porta Suero

EXPLICACION SIMBOLOGIA

Ancho vano — P1 / 80 — Tipo de puerta
Tipo de ventana — V1
Edificio — A2-101 — N° recinto — Piso
Dirección vista — Nombre — 2 / 1-035 — N° de plano
Cielo — 11 / 1 / 21 / 11 — Muros — Piso

SIMBOLOGIA SANITARIO

Lm1: Lavamanos de uso múltiple pequeño al muro	BAA: Bota aguas de aseo
Lm2: Lavamanos suspendido de uso general	BAC: Bota aguas clínico VC1: Vertedero Clínico
Lm3: Lavamanos suspendido de uso médico	Lp1: Lavaplatos acero inoxidable 80 cm.
Lm4: Lavamanos para discapacitados	Lp2: Lavaplatos acero inoxidable 110 cms.
Lm5: Lavamanos bajo cubierta	Lv1: Lavadero multiuso simple
Lm6: Lavamanos estudio angular	Lv2: Lavadero multiuso doble
WC1: Sanitario con fluxor	Lv3: Lavadero multiuso simple
WC2: Sanitario con fluxor antivandálico (oculto)	LVQ1: Lavamanos cirujano doble
Du1: Receptáculo de ducha cuadrado	A1/A3/A4/B8/C1/J1/K1/L1/M1/O1/P1/R3: Lavamanos Acero Inox. 50x50
Du2: Receptáculo de ducha semi circular	G2/I4: Lavadero industrial simple 80x70 C3/J2/K2/L2/M2/O2/P2: Lavadero industrial simple 70x60
T1: Tina de baño	K3: Lavadero industrial simple 100x70
T2: Tina de baño niños	C4/B7: Lavadero industrial doble 140x60 B7/I3: Lavadero industrial doble 140x70
LCH: Lavachata PCH: Porta lavachata	G3/N2/R4: Lavadero industrial doble 40x70
DY: Lavadero para yeso DE: Ducha Emergencia	H3: Lavadero industrial triple

RESUMEN ESPECIFICACION RECINTOS

CIELOS
1: Cielo Americano
2: Plancha Yeso Cartón
3: Enrasado
4: Enlucido
5: Especial
6: Glassboard
7: Metálico Registrable

MUROS
11: Pintura al Óleo
12: Pintura Epóxica
13: Porcelanato
14: Tabique vidriado (VIDRIO LAMINADO)
15: No se consulta
16: No se consulta
17: Revestimiento PVC Soldable
18: Cerámica
19: Madera
20a: Acero Inoxidable
20b: Acero Galvanizado
20E: Revestimiento tipo gold medal, de seguridad. 38 mm muros, 32mm pisos.

PISOS
21: Porcelanato
22: Caucho Virgen Alto Tráfico
23: Caucho Virgen Disipativo
24: Caucho Virgen Acústico
25: Vinílico Antideslizante
26: Baldosa Microvibrada
27: Alfombra (Alto Tráfico)
28: Radier Afinado
29: No se consulta
30: Madera
31: Horm. Afinado + Caucho Clorado
32: Piso Registrable
33: Losa Impermeabilizada
34: Franja Antideslizante
35: Limpiapiés

A1

Rev 1	01-09-2017	ENTREGA FINAL	VERSION CONSTRUCCION	HHK/IHH

0 1 3 5 7,5

MINISTERIO DE SALUD
SERVICIO DE SALUD COQUIMBO

GOBIERNO REGIONAL
REGIÓN DE COQUIMBO

MINISTERIO DE SALUD
SERVICIO DE SALUD COQUIMBO
SUBDIRECCIÓN ADMINISTRATIVA - SUBDEPTO. DE GESTION DE RECURSOS FISICOS
--UNIDAD TÉCNICA DEL PROYECTO--

PROYECTO:
DISEÑOS DE ARQUITECTURA HOSPITALARIA, INGENIERIA Y ESPECIALIDADES
NORMALIZACION HOSPITAL DE OVALLE
CODIGO B.I.P N° 20133773
AV. MANUEL PEÑAFIEL OLIVARES S/N - OVALLE - REGION DE COQUIMBO

ESPECIALIDAD: ARQUITECTURA
CONTENIDO LAMINA: Planta Edif. G 1°Piso

ESQUEMA DE UBICACION:

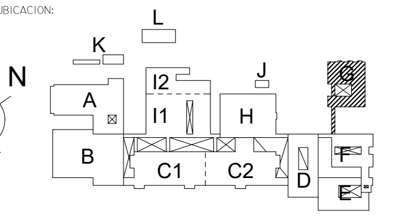

N° LAMINA:	1-132
ESCALA / FORM.: 1 : 75	FECHA: 01/09/2017
PROYECTO: HHK/IHH/CVBO	APROBACION: HHK
DIBUJO: H+A	ARCHIVO: NHO_1-124.dwg
N° CORRELATIVO: 032 DE 052	N° PROYECTO CONSULTOR: 265

CONTRATISTA:	PROPIETARIO:	ARQUITECTO:
EMPRESA CONSTRUCTORA	ERNESTO JORQUERA FLORES DIRECTOR SERVICIO DE SALUD COQUIMBO	IVÁN HILDEBRANDT HRASTE ARQUITECTO UTFSM REP. LEGAL HILDEBRANDT Y ASOC. A.I.C. LTDA.

hildebrandt planconsult®
HILDEBRANDT + ASOCIADOS
ARQUITECTOS INGENIEROS CONSULTORES LTDA.
BUCAREST 17, OF. 81, PROVIDENCIA, SANTIAGO DE CHILE
FONOS: (2) 2321 8582, 2333 9490 · FAX: (2) 2334 1114 · E-MAIL: PLANCONSULT@HILDEBRANDT.CL

ARQUITECTURA / COORD. GRAL.:
HERIBERTO F. HILDEBRANDT KLAPP
ARQUITECTO U.CH., (DIPL. ING.)
CONSULTOR GENERAL
IVAN HILDEBRANDT HRASTE
ARQUITECTO UTFSM.
JEFE DE PROYECTO / COORD. GRAL.
EFIC. ENERGETICA / EE.TT. / ARQUITECTURA
KAREEN SILVA HRASTE
ARQUITECTO U.CH.
COORDINACIÓN DE PROYECTO / ARQUITECTURA
CRISTIAN VON BECK OYARZUN
ARQUITECTO U.C.
ARQUITECTURA
JULIO SAAVEDRA QUIROZ
ARQUITECTO U.CH.
ARQUITECTURA
FRANCISCO ESCOBAR LAFFERTE
ARQUITECTO USACH
MAQUETA FISICA / ARQUITECTURA
YERKO CABRERA REYES
ARQUITECTO U.CH.
ARQUITECTURA

INGENIERIA / ESTUDIOS
MARCIAL BAEZA SETZ
INGENIERO CIVIL U.CH.
CÁLCULO ESTRUCTURAL
MANUEL RUZ JORQUERA
INGENIERO CIVIL U.CH.
MECÁNICA DE SUELOS
EDUARDO PASTÉN ROJAS
TÉCNICO EN TOPOGRAFÍA J.BOHON
TOPOGRAFÍA
GASTÓN FOURNIES LATORRE
M.SC., ING. CIVIL ELÉCTRICISTA UTFSM
I. ELECTRICIDAD / FUERZA
PATRICIA VUKASOVIK MAC LEAN
INGENIERO CIVIL UTFSM.
PAVIMENTACIÓN / A. LLUVIA
I. SANITARIAS / CO. INCENDIO / AGUAS LLUVIA / RIEGO AUT. / GAS LICUADO
ORIONE PORZIO BOZZOLO
INGENIERO CIVIL
I. GASES MÉDICOS

INSTALACIONES DOMICILIARIAS
JULIO GORMAZ VENEGAS
ING. ASHRAE, TEC. IND. U.T.E.
I. TÉRMICAS / CLIMATIZACIÓN
RAMIRO LABAYRU MARTÍNEZ
PH.D., ING. QUÍMICO A.P.M.
RESIDUOS SOLIDOS / LÍQUIDOS
PROTECC. RADIOL. / RAD. IONIZANTES
MÓNICA PÉREZ NOVOA
ARQUITECTO P.U.C.
ALEJANDRA RIVEROS HILDEBRANDT
ARQUITECTO U.V.
PAISAJISMO
GUILLERMO MENARES BARRALES
ING. CIVIL INDUSTRIAL U.C.V.
CIRCULACIÓN VERTICAL MECÁNICA
DOMINIQUE MUZARD LE MINIHY
DISEÑADORA P.U.C
MOBILIARIO ADOSADO
CARMEN GLORIA SIMPSON ALVAREZ
INGENIERO CIVIL U.CH.
IMPACTO VIAL Y DE TRÁNSITO

LUZ MARINA DELGADO
ING. CIVIL ELECTRÓNICO U.DE LA F.
I. CONTROL CENTRALIZ. / COMUNICACIONES
SIST. LLAMADA / CCTV./ CC.DD. / C.ACC.
WALDO VALDÉS ZÁRATE
INGENIERO MECÁNICO USACH
SISTEMAS DE SEGURIDAD
ALEJANDRA CANESSA V.
DISEÑADORA GRÁFICA U.M.
SEÑALETICA INTERIOR Y EXTERIOR
DANIEL BOSSONNEY CHAUVAUD
ING. CIVIL INDUSTRIAL USACH
I. CORREO NEUMÁTICO
LEONARDO PALMA SALAZAR
ARQUITECTO U. CH.
INSONORIZACIÓN
ROBERTO CALLEJAS CARRASCO
ING. CONSTRUCTOR U.C.V.
CUBICACIÓN Y PRESUPUESTO OFICIAL
PROG. DE EJECUCIÓN DE OBRAS
JORGE CONCHA O.
HELIPÚERTO

16-10-2014 13:00:02