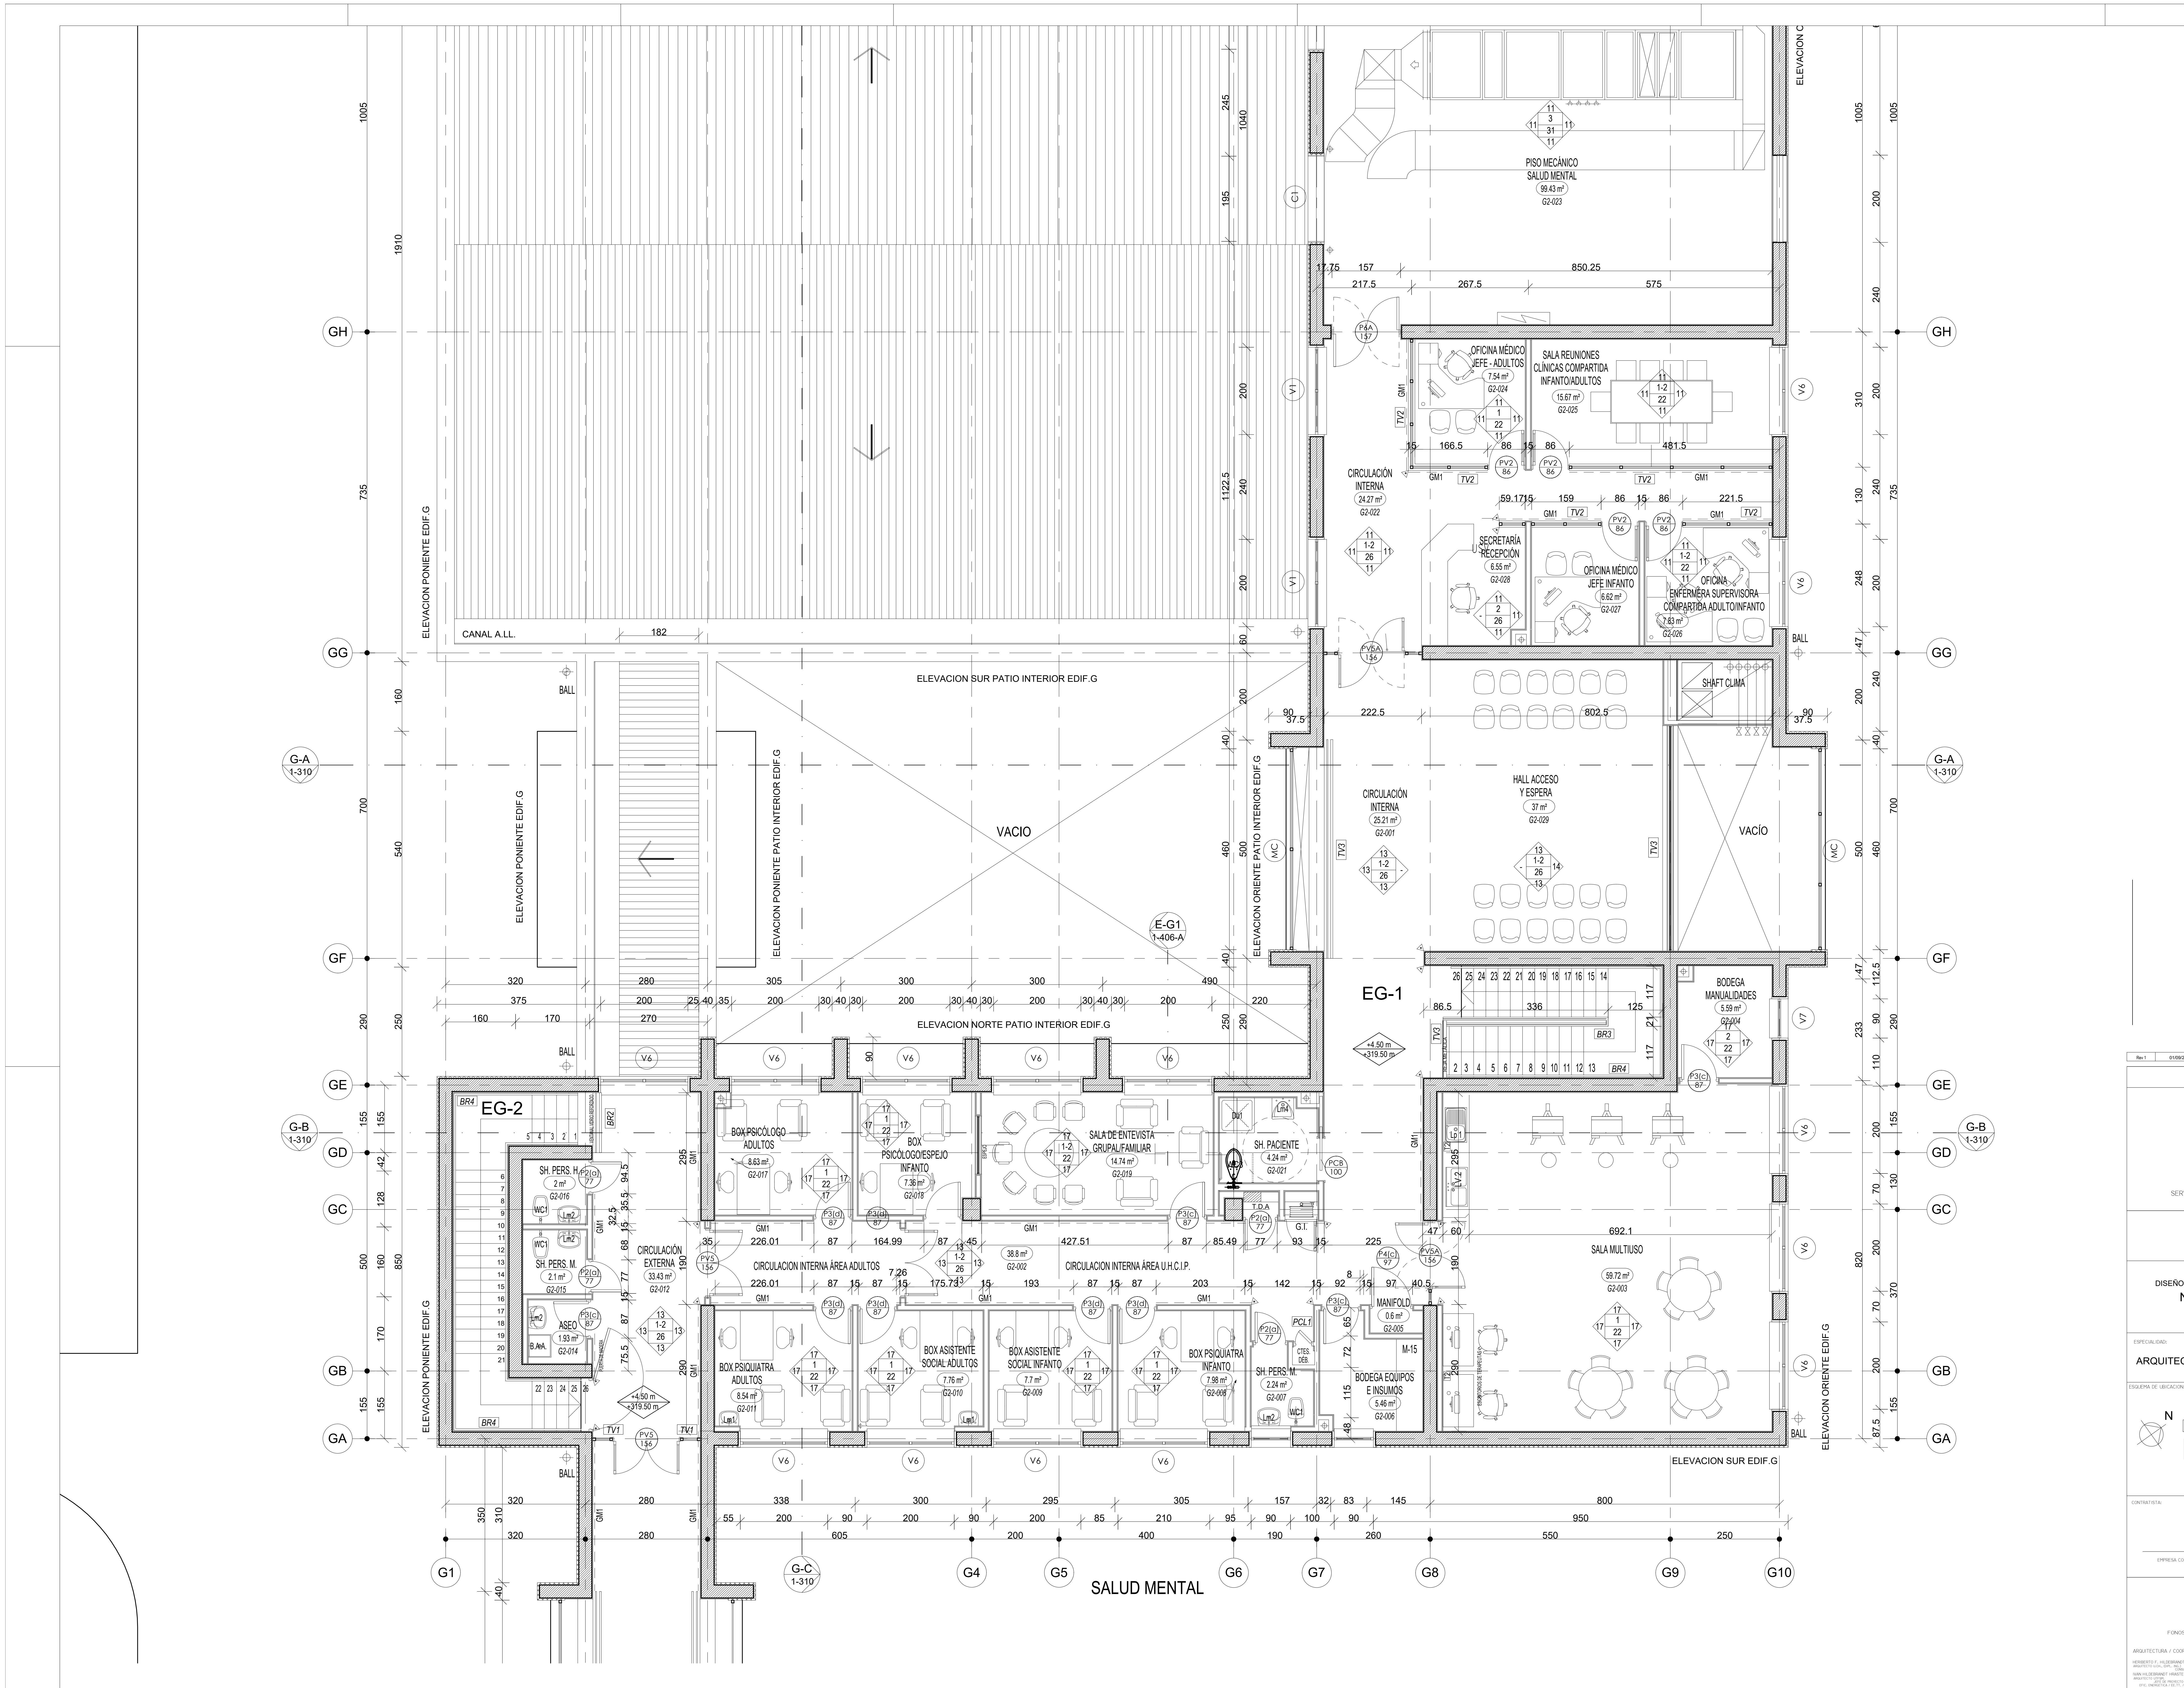
PISO MECÁNICO SALUD MENTAL 99.43 m² G2-023
OFICINA MÉDICO JEFE - ADULTOS 7.54 m² G2-024
SALA REUNIONES CLÍNICAS COMPARTIDA INFANTO/ADULTOS 15.67 m² G2-025
CIRCULACIÓN INTERNA 24.27 m² G2-022
SECRETARÍA RECEPCIÓN 6.55 m² G2-028
OFICINA MÉDICO JEFE INFANTO 8.62 m² G2-027
OFICINA ENFERMERA SUPERVISORA COMPARTIDA ADULTO/INFANTO 7.83 m² G2-026
SHAFT CLIMA
CANAL A.LL.
ELEVACION SUR PATIO INTERIOR EDIF.G
ELEVACION PONIENTE EDIF.G
ELEVACION PONIENTE PATIO INTERIOR EDIF.G
ELEVACION ORIENTE PATIO INTERIOR EDIF.G
VACIO
CIRCULACIÓN INTERNA 25.21 m² G2-001
HALL ACCESO Y ESPERA 37 m² G2-029
VACÍO
E-G1 1-406-A
EG-1
BODEGA MANUALIDADES 5.59 m² G2-004
ELEVACION NORTE PATIO INTERIOR EDIF.G
EG-2
+4.50 m +319.50 m
BOX PSICÓLOGO ADULTOS 8.63 m² G2-017
BOX PSICÓLOGO/ESPEJO INFANTO 7.36 m² G2-018
SALA DE ENTEVISTA GRUPAL/FAMILIAR 14.74 m² G2-019
SH. PACIENTE 4.24 m² G2-021
SH. PERS. H. 2 m² G2-016
SH. PERS. M. 2.1 m² G2-015
ASEO 1.93 m² G2-014
CIRCULACIÓN EXTERNA 33.43 m² G2-012
CIRCULACION INTERNA ÁREA ADULTOS
38.8 m² G2-002
CIRCULACION INTERNA ÁREA U.H.C.I.P.
MANIFOLD 0.6 m² G2-005
SALA MULTIUSO 59.72 m² G2-003
BOX PSIQUIATRA ADULTOS 8.54 m² G2-011
BOX ASISTENTE SOCIAL ADULTOS 7.76 m² G2-010
BOX ASISTENTE SOCIAL INFANTO 7.7 m² G2-009
BOX PSIQUIATRA INFANTO 7.58 m² G2-008
SH. PERS. M. 2.24 m² G2-007
BODEGA EQUIPOS E INSUMOS 5.46 m² G2-006
ELEVACION SUR EDIF.G
ELEVACION ORIENTE EDIF.G
GH
GG
G-A 1-310
GF
GE
G-B 1-310
GD
GC
GB
GA
G1
G-C 1-310
G4
G5
G6
G7
G8
G9
G10
SALUD MENTAL

Planta Edif. G, 2º Piso

ESCALA 1:50

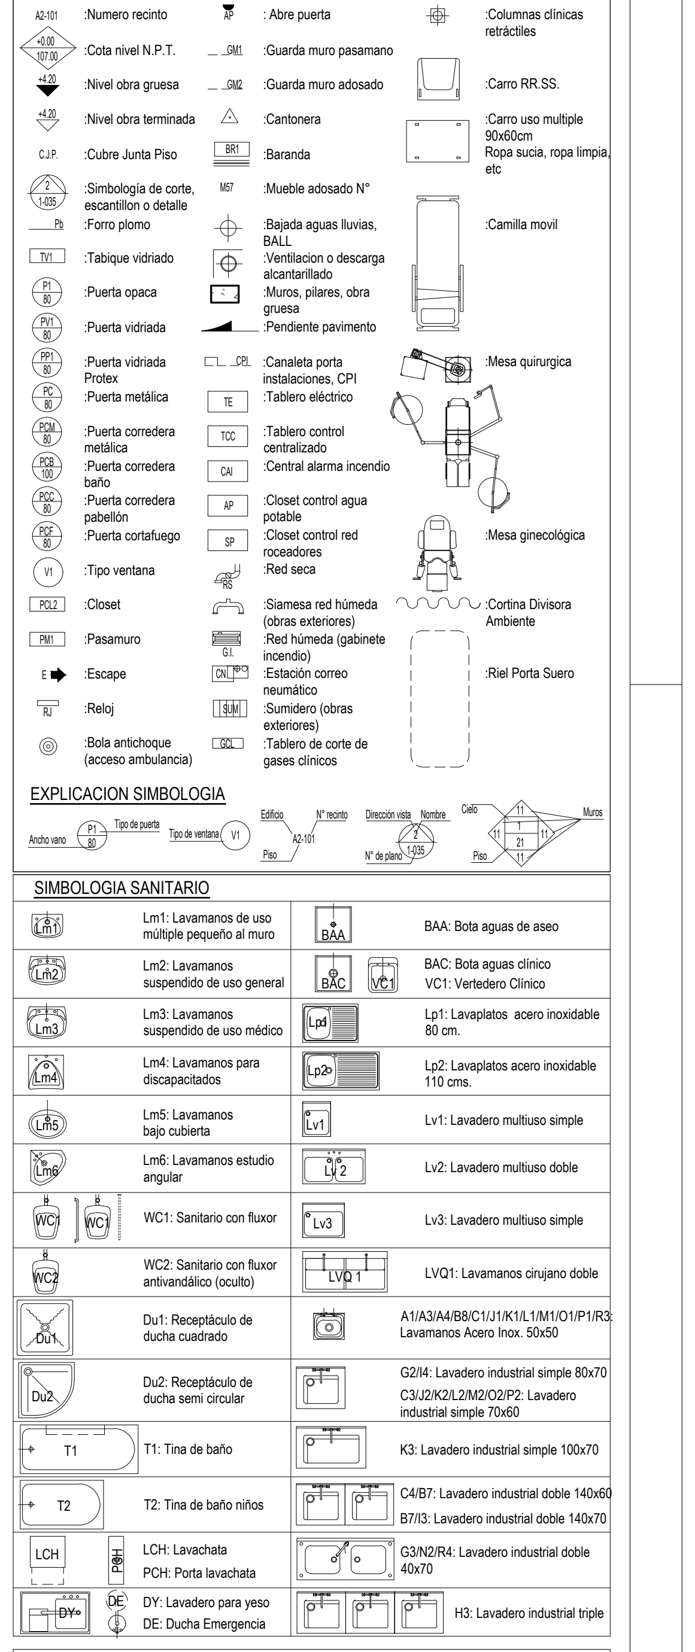
SIMBOLOGIA
SIMBOLOGIA GENERAL
A2-101 :Numero recinto
:Cota nivel N.P.T.
:Nivel obra gruesa
:Nivel obra terminada
C.J.P. :Cubre Junta Piso
:Simbología de corte, escantillon o detalle
Pb :Forro plomo
TV1 :Tabique vidriado
P1 80 :Puerta opaca
PV1 80 :Puerta vidriada
PP1 80 :Puerta vidriada Protex
PC 80 :Puerta metálica
PCM 80 :Puerta corredera metálica
PCB 100 :Puerta corredera baño
PCC 80 :Puerta corredera pabellón
PCF 80 :Puerta cortafuego
V1 :Tipo ventana
PCL2 :Closet
PM1 :Pasamuro
E :Escape
RJ :Reloj
:Bola antichoque (acceso ambulancia)
AP : Abre puerta
GM1 :Guarda muro pasamano
GM2 :Guarda muro adosado
:Cantonera
BR1 :Baranda
M57 :Mueble adosado N°
:Bajada aguas lluvias, BALL
:Ventilacion o descarga alcantarillado
:Muros, pilares, obra gruesa
:Pendiente pavimento
CPI :Canaleta porta instalaciones, CPI
TE :Tablero eléctrico
TCC :Tablero control centralizado
CAI :Central alarma incendio
AP :Closet control agua potable
SP :Closet control red roceadores
RS :Red seca
:Siamesa red húmeda (obras exteriores)
G.I. :Red húmeda (gabinete incendio)
CN :Estación correo neumático
SUM :Sumidero (obras exteriores)
GCL :Tablero de corte de gases clínicos
:Columnas clínicas retráctiles
:Carro RR.SS.
:Carro uso multiple 90x60cm Ropa sucia, ropa limpia, etc
:Camilla movil
:Mesa quirurgica
:Mesa ginecológica
:Cortina Divisora Ambiente
:Riel Porta Suero
EXPLICACION SIMBOLOGIA
Ancho vano
Tipo de puerta
Tipo de ventana
Edificio
N° recinto
Piso
Dirección vista
Nombre
N° de plano
Cielo
Muros
Piso
SIMBOLOGIA SANITARIO
Lm1: Lavamanos de uso múltiple pequeño al muro
BAA: Bota aguas de aseo
Lm2: Lavamanos suspendido de uso general
BAC: Bota aguas clínico
VC1: Vertedero Clínico
Lm3: Lavamanos suspendido de uso médico
Lp1: Lavaplatos acero inoxidable 80 cm.
Lm4: Lavamanos para discapacitados
Lp2: Lavaplatos acero inoxidable 110 cms.
Lm5: Lavamanos bajo cubierta
Lv1: Lavadero multiuso simple
Lm6: Lavamanos estudio angular
Lv2: Lavadero multiuso doble
WC1: Sanitario con fluxor
Lv3: Lavadero multiuso simple
WC2: Sanitario con fluxor antivandálico (oculto)
LVQ1: Lavamanos cirujano doble
Du1: Receptáculo de ducha cuadrado
A1/A3/A4/B8/C1/J1/K1/L1/M1/O1/P1/R3: Lavamanos Acero Inox. 50x50
Du2: Receptáculo de ducha semi circular
G2/I4: Lavadero industrial simple 80x70
C3/J2/K2/L2/M2/O2/P2: Lavadero industrial simple 70x60
T1: Tina de baño
K3: Lavadero industrial simple 100x70
T2: Tina de baño niños
C4/B7: Lavadero industrial doble 140x60
B7/I3: Lavadero industrial doble 140x70
LCH: Lavachata
PCH: Porta lavachata
G3/N2/R4: Lavadero industrial doble 40x70
DY: Lavadero para yeso
DE: Ducha Emergencia
H3: Lavadero industrial triple

RESUMEN ESPECIFICACION RECINTOS

CIELOS	MUROS	PISOS
1: Cielo Americano	11: Pintura al Óleo	21: Porcelanato
2: Plancha Yeso Cartón	12: Pintura Epóxica	22: Caucho Virgen Alto Tráfico
3: Enrasado	13: Porcelanato	23: Caucho Virgen Disipativo
4: Enlucido	14: Tabique vidriado	24: Caucho Virgen Acústico
5: Especial	15: No se consulta	25: Vinílico Antideslizante
6: Glassboard	16: No se consulta	26: Baldosa Microvibrada
7: Metálico Registrable	17: Revestimiento PVC Soldable	27: Alfombra (Alto Tráfico)
	18: Cerámica	28: Radier Afinado
	19: Madera	29: No se consulta
	20a: Acero Inoxidable	30: Madera
	20b: Acero Galvanizado	31: Horm. Afinado + Caucho Clorado
		32: Piso Registrable
		33: Losa Impermeabilizada
		34: Franja Antideslizante
		35: Limpiapiés

SS.HH., ASEO, BODEGA, CLOSET, OFICINA MEDICO JEFE

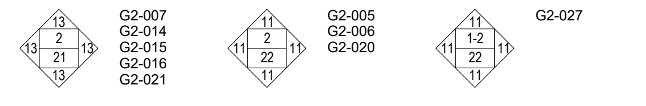

G2-007
G2-014
G2-015
G2-016
G2-021

G2-005
G2-006
G2-020

G2-027

Rev 1	01/09/2017	ENTREGA FINAL	VERSION CONSTRUCCION	HHK/IHH

0 1 3 5 7,5

MINISTERIO DE SALUD
SERVICIO DE SALUD COQUIMBO

GOBIERNO REGIONAL
REGIÓN DE COQUIMBO

MINISTERIO DE SALUD
SERVICIO DE SALUD COQUIMBO

SUBDIRECCIÓN ADMINISTRATIVA - SUBDEPTO. DE GESTION DE RECURSOS FISICOS
--UNIDAD TÉCNICA DEL PROYECTO--

PROYECTO:
DISEÑOS DE ARQUITECTURA HOSPITALARIA, INGENIERIA Y ESPECIALIDADES
NORMALIZACION HOSPITAL DE OVALLE
CODIGO B.I.P N° 20133773
AV. MANUEL PEÑAFIEL OLIVARES S/N - OVALLE - REGION DE COQUIMBO

ESPECIALIDAD: ARQUITECTURA

CONTENIDO LAMINA: Planta Edif. G 2°Piso

ESQUEMA DE UBICACION:

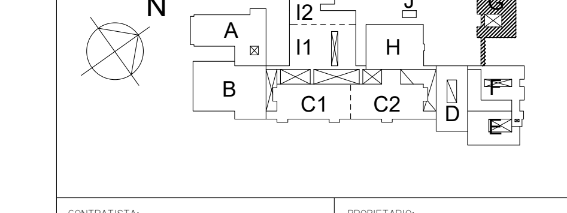

N° LAMINA: 1-133

ESCALA / FORM.: 1:50/ FORM.: A0

FECHA: 01/09/2017

PROYECTO: HHK/IHH/CVBO

APROBACION: CSS

DIBUJO:

ARCHIVO:

N° CORRELATIVO:

N° PROYECTO CONSULTOR: 265

CONTRATISTA:
EMPRESA CONSTRUCTORA

PROPIETARIO:
ERNESTO JORQUERA FLORES
DIRECTOR SERVICIO DE SALUD COQUIMBO

ARQUITECTO:
IVÁN HILDEBRANDT HRASTE
ARQUITECTO UTFSM
REP. LEGAL HILDEBRANDT Y ASOC. A.I.C. LTDA.

hildebrandt planconsult®
HILDEBRANDT + ASOCIADOS
ARQUITECTOS INGENIEROS CONSULTORES LTDA.
BUCAREST 17, OF. 81, PROVIDENCIA, SANTIAGO DE CHILE
FONOS: (2) 2321 8582, 2333 9490 · FAX: (2) 2334 1114 · E-MAIL: PLANCONSULT@HILDEBRANDT.CL

ARQUITECTURA / COORD. GRAL.:
HERIBERTO F. HILDEBRANDT KLAPP
ARQUITECTO U.CH., (DIPL. ING.)
CONSULTOR GENERAL
IVAN HILDEBRANDT HRASTE
ARQUITECTO UTFSM.
JEFE DE PROYECTO / COORD. GRAL.
EFIC. ENERGETICA / EE.TT. / ARQUITECTURA
KAREEN SILVA HRASTE
ARQUITECTO U.CH.
COORDINACIÓN DE PROYECTO / ARQUITECTURA
CRISTIAN VON BECK OYARZUN
ARQUITECTO U.C.
ARQUITECTURA
JULIO SAAVEDRA QUIROZ
ARQUITECTO U.CH.
ARQUITECTURA
FRANCISCO ESCOBAR LAFFERTE
ARQUITECTO USACH
MAQUETA FISICA / ARQUITECTURA
YERKO CABRERA REYES
ARQUITECTO U.CH.
ARQUITECTURA

INGENIERIA / ESTUDIOS
MARCIAL BAEZA SETZ
INGENIERO CIVIL U.CH.
CÁLCULO ESTRUCTURAL
MANUEL RUZ JORQUERA
INGENIERO CIVIL U.CH.
MECÁNICA DE SUELOS
EDUARDO PASTÉN ROJAS
TÉCNICO EN TOPOGRAFÍA J.BOHON
TOPOGRAFÍA
GASTÓN FOURNIES LATORRE
M.SC., ING. CIVIL ELÉCTRICISTA UTFSM
I. ELECTRICIDAD / FUERZA
PATRICIA VUKASOVIK MAC LEAN
INGENIERO CIVIL UTFSM.
PAVIMENTACIÓN / A. LLUVIA
I. SANITARIAS / CO. INCENDIO / AGUAS LLUVIA / RIEGO AUT. / GAS LICUADO
ORIONE PORZIO BOZZOLO
INGENIERO CIVIL
I. GASES MÉDICOS

INSTALACIONES DOMICILIARIAS
JULIO GORMAZ VENEGAS
ING. ASHRAE, TEC. IND. U.T.E.
I. TÉRMICAS / CLIMATIZACIÓN
RAMIRO LABAYRU MARTÍNEZ
PH.D., ING. QUÍMICO A.P.M.
RESIDUOS SOLIDOS / LÍQUIDOS
PROTECC. RADIOL. / RAD. IONIZANTES
MÓNICA PÉREZ NOVOA
ARQUITECTO P.U.C.
ALEJANDRA RIVEROS HILDEBRANDT
ARQUITECTO U.V.
PAISAJISMO
GUILLERMO MENARES BARRALES
ING. CIVIL INDUSTRIAL U.C.V.
CIRCULACIÓN VERTICAL MECÁNICA
DOMINIQUE MUZARD LE MINIHY
DISEÑADORA P.U.C
MOBILIARIO ADOSADO
CARMEN GLORIA SIMPSON ALVAREZ
INGENIERO CIVIL U.CH.
IMPACTO VIAL Y DE TRÁNSITO

LUZ MARINA DELGADO
ING. CIVIL ELECTRÓNICO U.DE LA F.
I. CONTROL CENTRALIZ. / COMUNICACIONES
SIST. LLAMADA / CCTV./ CC.DD. / C.ACC.
WALDO VALDÉS ZÁRATE
INGENIERO MECÁNICO USACH
SISTEMAS DE SEGURIDAD
ALEJANDRA CANESSA V.
DISEÑADORA GRÁFICA U.M.
SEÑALETICA INTERIOR Y EXTERIOR
DANIEL BOSSONNEY CHAUVAUD
ING. CIVIL INDUSTRIAL USACH
I. CORREO NEUMÁTICO
LEONARDO PALMA SALAZAR
ARQUITECTO U. CH.
INSONORIZACIÓN
ROBERTO CALLEJAS CARRASCO
ING. CONSTRUCTOR U.C.V.
CUBICACIÓN Y PRESUPUESTO OFICIAL
PROG. DE EJECUCIÓN DE OBRAS
JORGE CONCHA O.
HELIPÚERTO